


Stage 3 Annotated Points

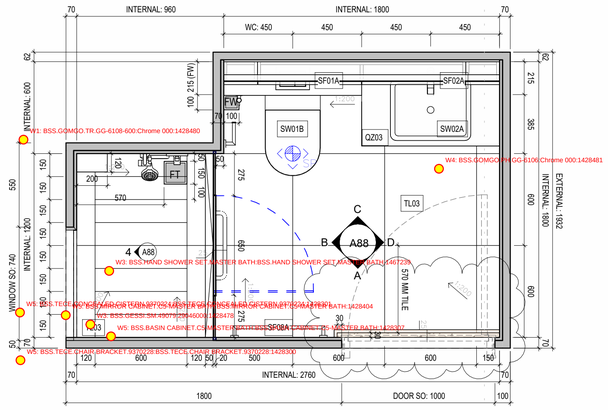


1 FINISHED FLOOR LEVEL
1 : 20

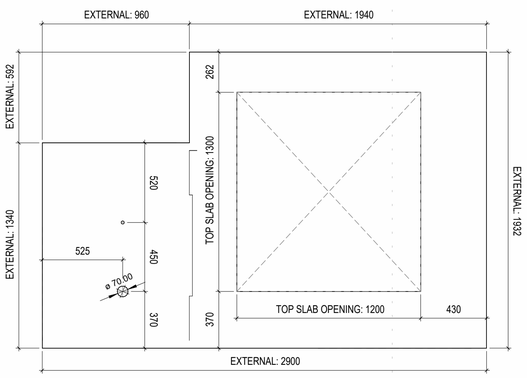


2 CEILING LEVEL
1 : 20

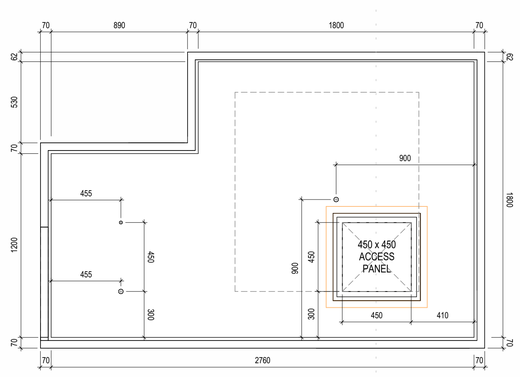


3 REFLECTED CEILING PLAN
1 : 20

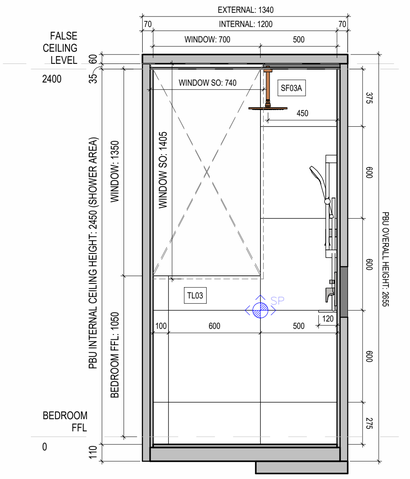


4 SHOWER AREA
1 : 20

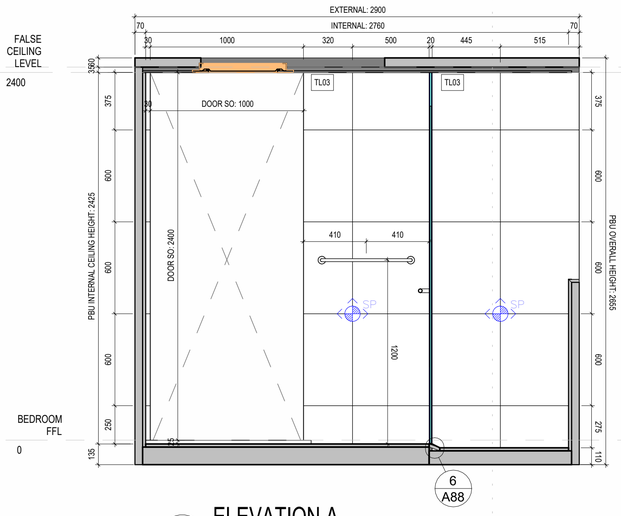


A ELEVATION A
1 : 20

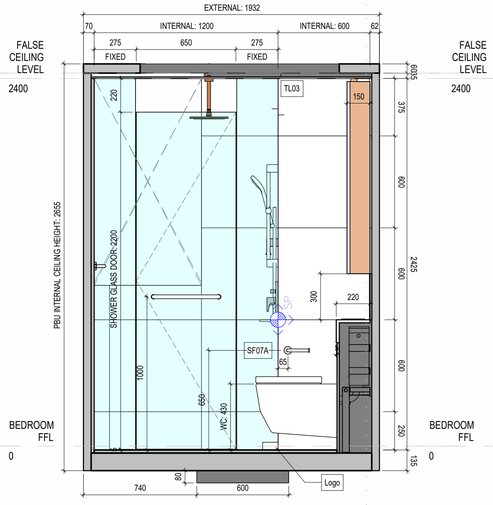


B ELEVATION B
1 : 20

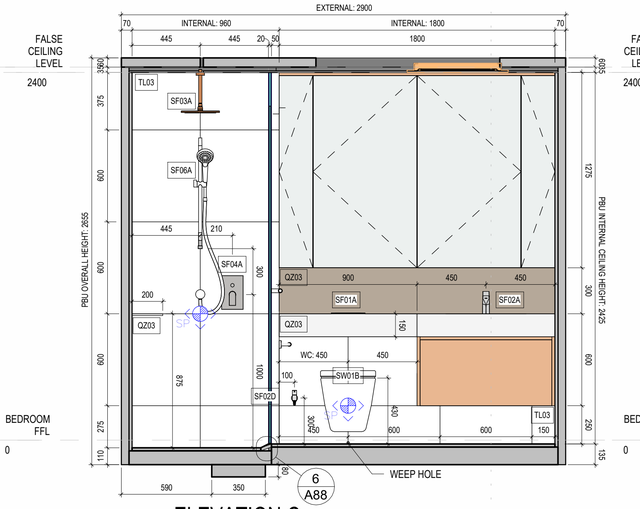


C ELEVATION C
1 : 20

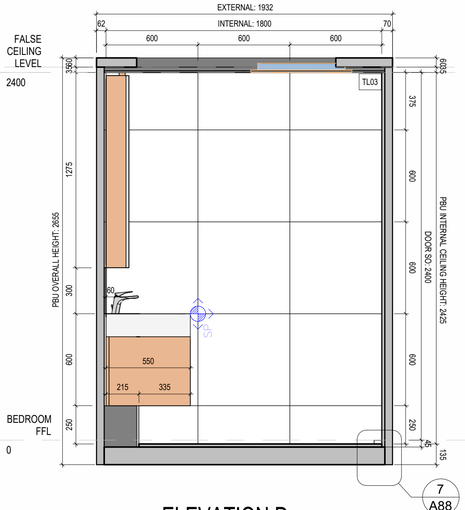


D ELEVATION D
1 : 20

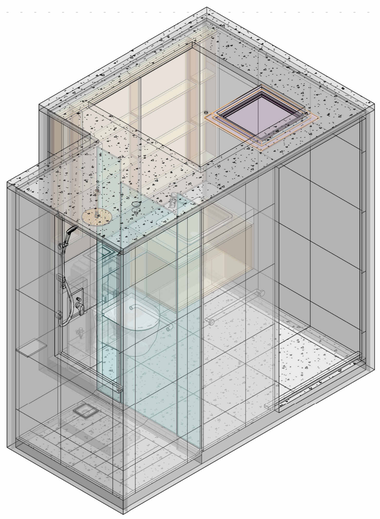


5 3D VIEW 1

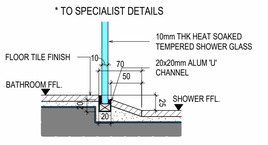


6 DETAIL A
1 : 5

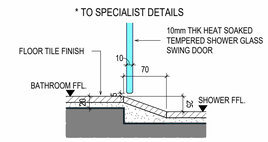

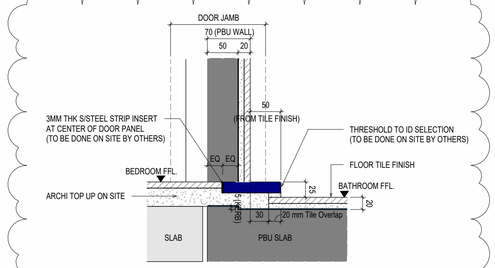

7 FLOOR THRESHOLD
1 : 5

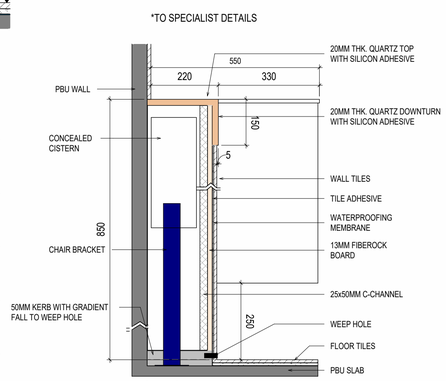

8 WC LOW WALL
1 : 10

SCHEDULE OF FINISHES	
CODE	DESCRIPTION
TL03	APPLICATION: WALL / FLOOR SIZE: 600 x 600 MM MODEL: CERAMIC / PORCELAIN TILE IN NATURAL FINISH SHOWER FLOOR AREA TO CUT TO 150 x 600MM
QZ03	APPLICATION: VANITY BACKPLASH, SHOWER LEDGE THICKNESS: 12MM APPLICATION: VANITY TOP THICKNESS: 20MM MODEL: COMPRESSED QUARTZ (SILESTONE - DESSERT SILVER) IN SUEDE FINISH

PBU APPLICABLE FOR:				
BLOCK	LEVEL	UNIT TYPE	UNIT NO.	PBU TYPE
3(18B)	5	E3-PH	22	JMB
4(22)	5	E2-PH(M)	36	

SCHEDULE OF SANITARY WARES

S/N	IMAGE	REMARKS	LEGEND
01		SOLFERINO BASIN MIXER, WITH WASTE (CHROME) BRAND: GESSI MODEL: 49001-031	SF02A
02		PRO S UNDERCOUNTER WASH BASIN SIZE: L530 x W400 x D170 MM BRAND: LAUFEN MODEL: 8.1196.1.000.109.1	SW02A
03		BASAL WALL HUNG RIMLESS WC SIZE: W360 x D530 x H350 MM BRAND: LAUFEN MODEL: 8.2071.4.000.024.1	SW01B
04		CONCEALED CISTERN + CHAIR BRACKETS BRAND: TECE MODEL: 9370224 + 9370228	
05		TECE NOW FLUSH ACTUATOR BRAND: TECE MODEL: 9240402	SF01A
06		SOLFERINO CONCEALED BATH MIXER BRAND: GESSI MODEL: 49079-031	SF04A

S/N	IMAGE	REMARKS	LEGEND
07		EMPORIO SHOWER SET, HANDSHOWER 100 BRAND: GESSI MODEL: 47306-031	SF06A
08		INGRANAGGIO CEILING-MOUNTED ADJUSTABLE SHOWERHEAD BRAND: GESSI MODEL: 63352-031	SF03A
09		BIB TAP BRAND: MONIC MODEL: T-4D-3	SF02D
10		BATH TOWEL RAIL BRAND: GOMGO MODEL: GG-6108-600	SF08A
11		PAPER ROLL HOLDER BRAND: GOMGO MODEL: GG-6106	SF07A

SHOP DRAWING

P&T COSULTANTS PTE LTD

SHOP DRAWINGS REVIEW

The Examination of this sample / shop drawing is made to check compliance with the requirements of the contract conditions, specifications and contract drawings. Comments, corrections, and approval made on the shop drawing / sample by the architect do not relieve the contractor of his contractual responsibilities and from compliance with requirements of the contract conditions, specifications, and contract drawings, including design responsibility where expressly required. This check only for the review of general conformance with the design concept of the project general compliance with the design intent of the specifications and drawings. No claims by the contractor for extra payment based on the shop drawing / sample shall be considered unless such cases, if any, are noted on the contractor's transmittal letter accompanying this drawing and will then be subjected to decision of the architect or quantity surveyor.

☐ No exception taken ☐ To amend and resubmit
☐ Make correction noted ☐ Rejected (see remarks)
Name/Sign: ..... Date: .....

SHOP DRAWINGS REVIEW

Comments/Corrections made on this shop drawings does not relieve the Contractor(s)/Sub-Contractor(s) of the responsibility for ensuring full compliance with all requirement of the contract, specifications and documents.

The Contractor(s)/Sub-Contractor(s) is responsible for all dimensions which shall be confirmed and correlated at the job site, fabrication processes, techniques of construction and co-coodination of his/her work with that of all other trades.

MEINHARDT (SINGAPORE) PTE LTD

This drawing is returned to the Contractor for the following action:

☐ No exception taken ☐ To amend and resubmit
☐ Make correction noted ☐ Rejectd (see remarks)
Name/ Sign: Date:

UNITED PROJECT CONSULTANTS PTE LTD

This drawing is returned to the Contractor for the following action:

☐ No exception taken ☐ To amend and resubmit
☐ Make correction noted ☐ Rejectd (see remarks)
Name/ Sign: Date:

2ND EDITION PTE LTD

This drawing is returned to the Contractor for the following action:

☐ No exception taken ☐ To amend and resubmit
☐ Make correction noted ☐ Rejectd (see remarks)
Name/ Sign: Date:

SITETECTONIX PTE LTD

This drawing is returned to the Contractor for the following action:

☐ No exception taken ☐ To amend and resubmit
☐ Make correction noted ☐ Rejectd (see remarks)
Name/ Sign: Date:

REV	DATE	SUBJECT	CHKD
0	-		
1	12/8/24	REVISED DOOR LOCATION	
2	13/8/24	ADJUSTED PBU LAYOUT	BSS
3	20/11/24	REVISED THRESHOLD DETAIL	

DEVELOPER:
HOI HUP REALTY SUNWAY
HOI HUP SUNWAY KENT RIDGE PTE LTD
16 JALAN KILANG #07-01 HOI HUP BUILDING SINGAPORE 159416
TEL: 6311 9555 FAX: 6271 9282

ARCHITECT:
P&T CONSULTANTS PTE LTD
150 BEACH ROAD #07-01/08 GATEWAY WEST SINGAPORE 3189720
TEL: 6535 2011 FAX: 6309 0339

CIVIL & STRUCTURAL ENGINEER:
MEINHARDT (SINGAPORE) PTE LTD
168 JALAN BUKIT MERAH #09-01, CONNECTION ONE SINGAPORE 150168
TEL: 6373 5255 FAX: 6274 0788

MECHANICAL & ELECTRICAL ENGINEER:
UNITED PROJECT CONSULTANTS PTE LTD
432 BALESTIER ROAD #02-444 PUBLIC MANSION SINGAPORE 298135
TEL: 6255 3900 FAX: 6253 4106

INTERIOR DESIGNER:
2ND EDITION PTE LTD
BCA BRADDELL CAMPUS BLOCK D #05-51 200 BRADDELL ROAD SINGAPORE 579700
TEL: 6298 8829

LANDSCAPE ARCHITECT:
SITETECTONIX PRIVATE LIMITED
60 ALBERT STREET #16-08 OG ALBERT COMPLEX SINGAPORE 189969
TEL: 6327 4452

MAIN CONTRACTOR:
Straits Construction Higher Further Together
STRAITS CONSTRUCTION SINGAPORE PTE LTD
16 JALAN KILANG #05-01 HOI HUP BUILDING SINGAPORE 159416
TEL: (65) 6222 6722 FAX: (65) 6222 6033
WEBSITE: www.straitsconstruction.com

SUBCONTRACTOR:
Bathsystem®
BATHSYSTEM SINGAPORE PTE LTD
21/23 KAKI BUKIT ROAD 6 #03-01 GREYFORM BUILDING SINGAPORE 415806
TEL: 6812 7777

PROJECT TITLE:
PROPOSED RESIDENTIAL FLAT DEVELOPMENT COMPRISING 9 BLOCKS OF 5-STOREY BUILDING (TOTAL 270 UNITS) WITH ATTIC, 1 LEVEL OF BASEMENT CARPARK, SWIMMING POOL AND COMMUNAL FACILITIES ON LOT 02062L MK 03 AT YEW SIANG ROAD (QUEENSTOWN PLANING AREA)

DRAWING TITLE:
PBU TYPE FP-MB-T1am(JMB)
(JUNIOR MASTER BATH)

DRAWN BY: WQ	SCALE: As indicated (A1)
CHKD BY: AR PL / ST PL / ME PL	DATE: 20 NOV 2024
APPROVED BY: AH	MODEL REF:
DRAWING No. TERRAHL2-FP-MB-T1am(JMB) -A88	REV. 3

THE OWNERSHIP OF THE COPYRIGHT IN THIS DRAWING IS RETAINED BY STRAITS CONSTRUCTION SINGAPORE PTE LTD WHOSE CONSENT MUST BE SOUGHT BEFORE ANY USE OF REPRODUCTION OF THE DRAWING OR ANY PART THEREOF CAN BE MADE.

A1 Template v20181212

P:\Bathsystem\40_TERRAHL2\2. CD (Coordinated Phase)\BIM\MDL\AR\TERRAHL2-FP-MB-T1am(JMB)-A88_4.rvt